

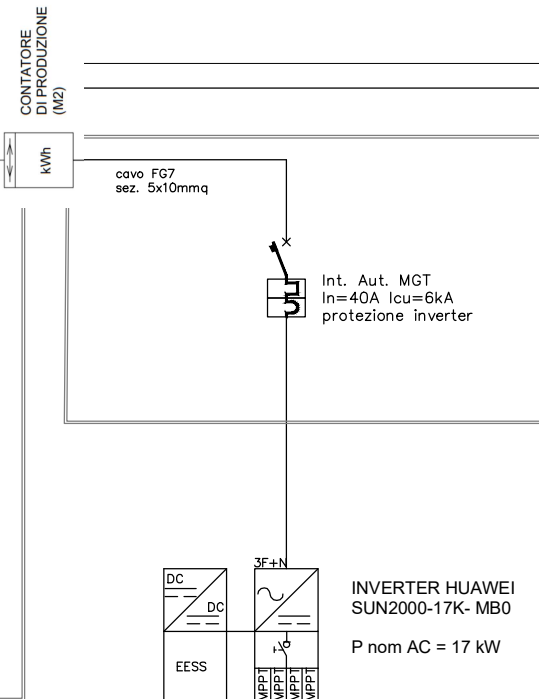
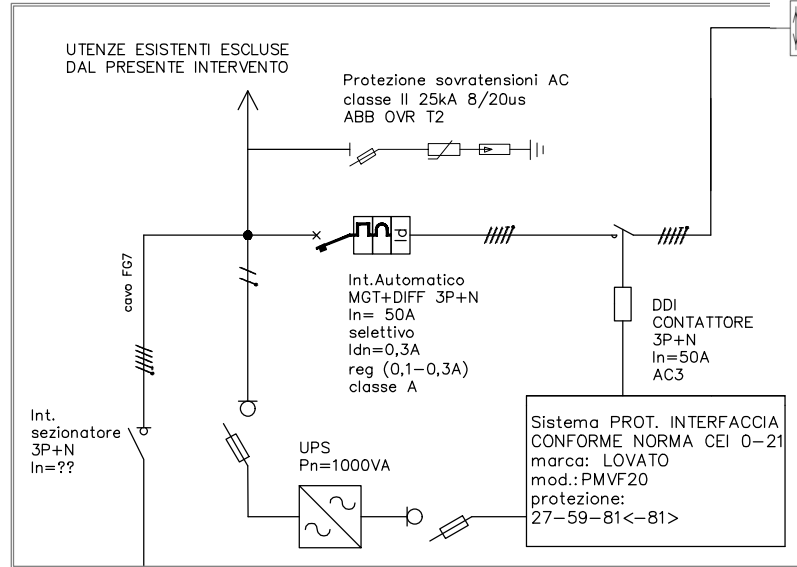


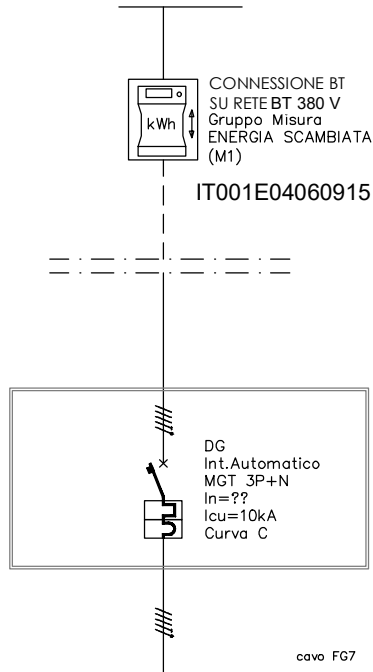

SISTEMA DI ACCUMULO
COMPOSTO DA
N. 2 BATTERIE
HUAWEI LUNA2000-14-S1
P netta = 13,8 kWh
P lorda = 13,8 kWh
P SdA = 7 kW

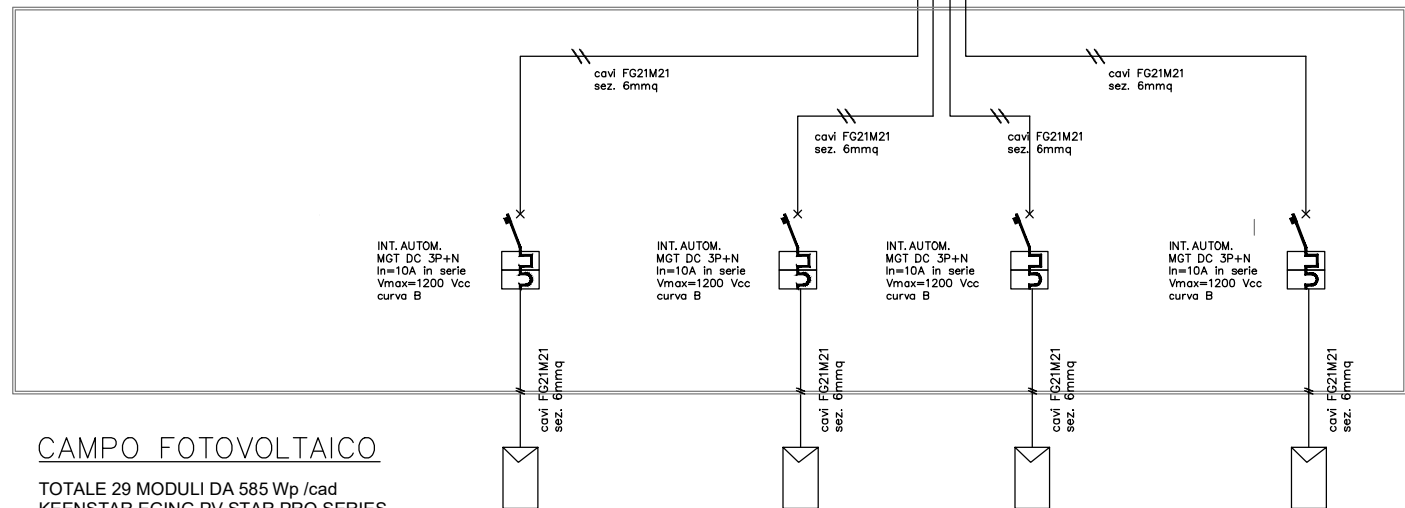

CAMPO FOTOVOLTAICO

TOTALE 29 MODULI DA 585 Wp /cad
KEENSTAR EGING PV STAR PRO SERIES

Pmax DC = 16,965 kW

AZING

INGEGNERIA SRL

Committente	TRATTORIA CANELLA S.N.C. P. A: 00885010249 VIA ROMA 25 36047 MONTEGALDELLA (VI)	Fase progetto PRELIMINARE
Indirizzo	SCHEMA ELETTRICO	Categoria lavoro PRELIMINARE
Oggetto	PRELIMINARE	Tavola 01
Descrizione	ING ALESSANDRO ZUANETTI	Piano/scala .
Progettista		Revisione 00
		Disegnatore A.Z.

REV	DATA	DESCRIZIONE	VER	DATA	VAL	DATA
00	09/07/25	UNIFILARE	A.Z.	09/07/25	A.Z.	09/07/25

Il presente disegno è di proprietà riservata. E' vietata la
riproduzione senza autorizzazione

Alessandro Zuanetti

