


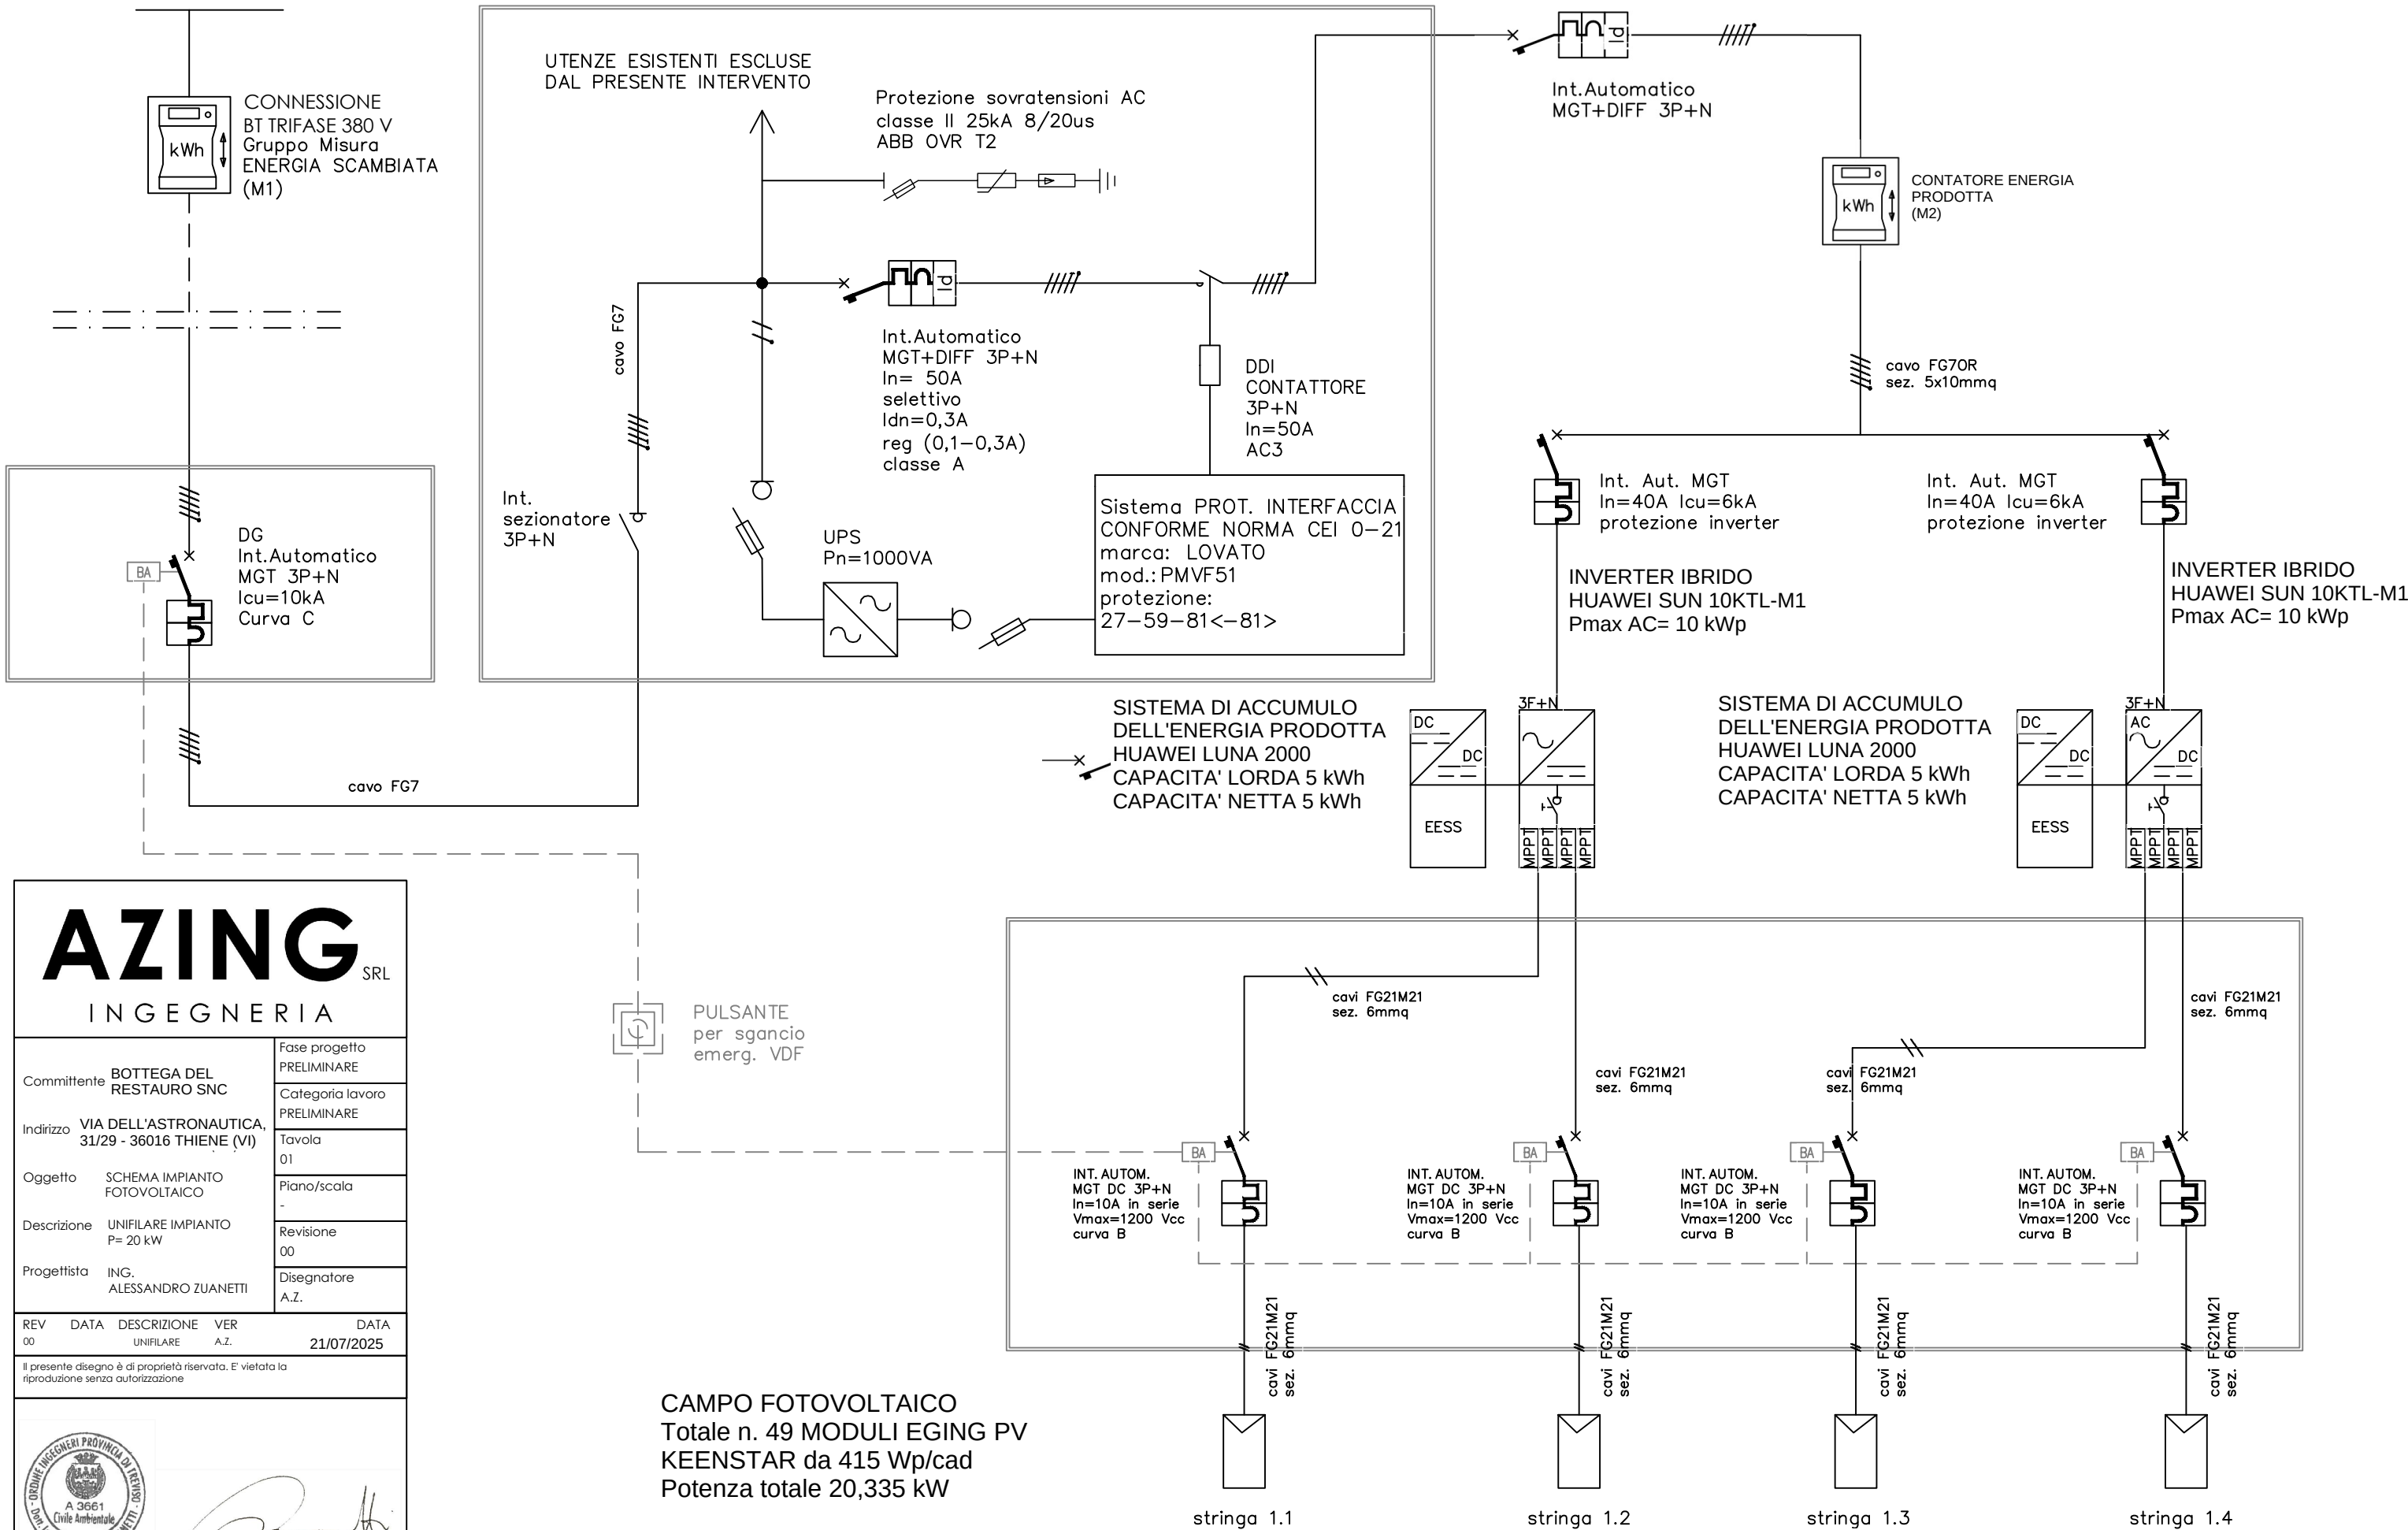

AZING

SRL

INGEGNERIA

Committente

BOTTEGA DEL RESTAURO SNC

Indirizzo

VIA DELL'ASTRONAUTICA, 31/29 - 36016 THIENE (VI)

Oggetto

SCHEMA IMPIANTO FOTOVOLTAICO

Descrizione

UNIFILARE IMPIANTO P= 20 kW

Progettista

ING. ALESSANDRO ZUANETTI

Fase progetto

PRELIMINARE

Categoria lavoro

PRELIMINARE

Tavola

01

Piano/scala

-

Revisione

00

Disegnatore

A.Z.

REV

00

DATA

00

DESCRIZIONE

UNIFILARE

VER

A.Z.

DATA

21/07/2025

Il presente disegno è di proprietà riservata. E' vietata la riproduzione senza autorizzazione

ORDINE INGEGNERI PROVINCIA DI TREVISO

A 3661

Civile Ambientale

Ing. ALESSANDRO ZUANETTI

CAMPO FOTOVOLTAICO
Totale n. 49 MODULI EGING PV
KEENSTAR da 415 Wp/cad
Potenza totale 20,335 kW