


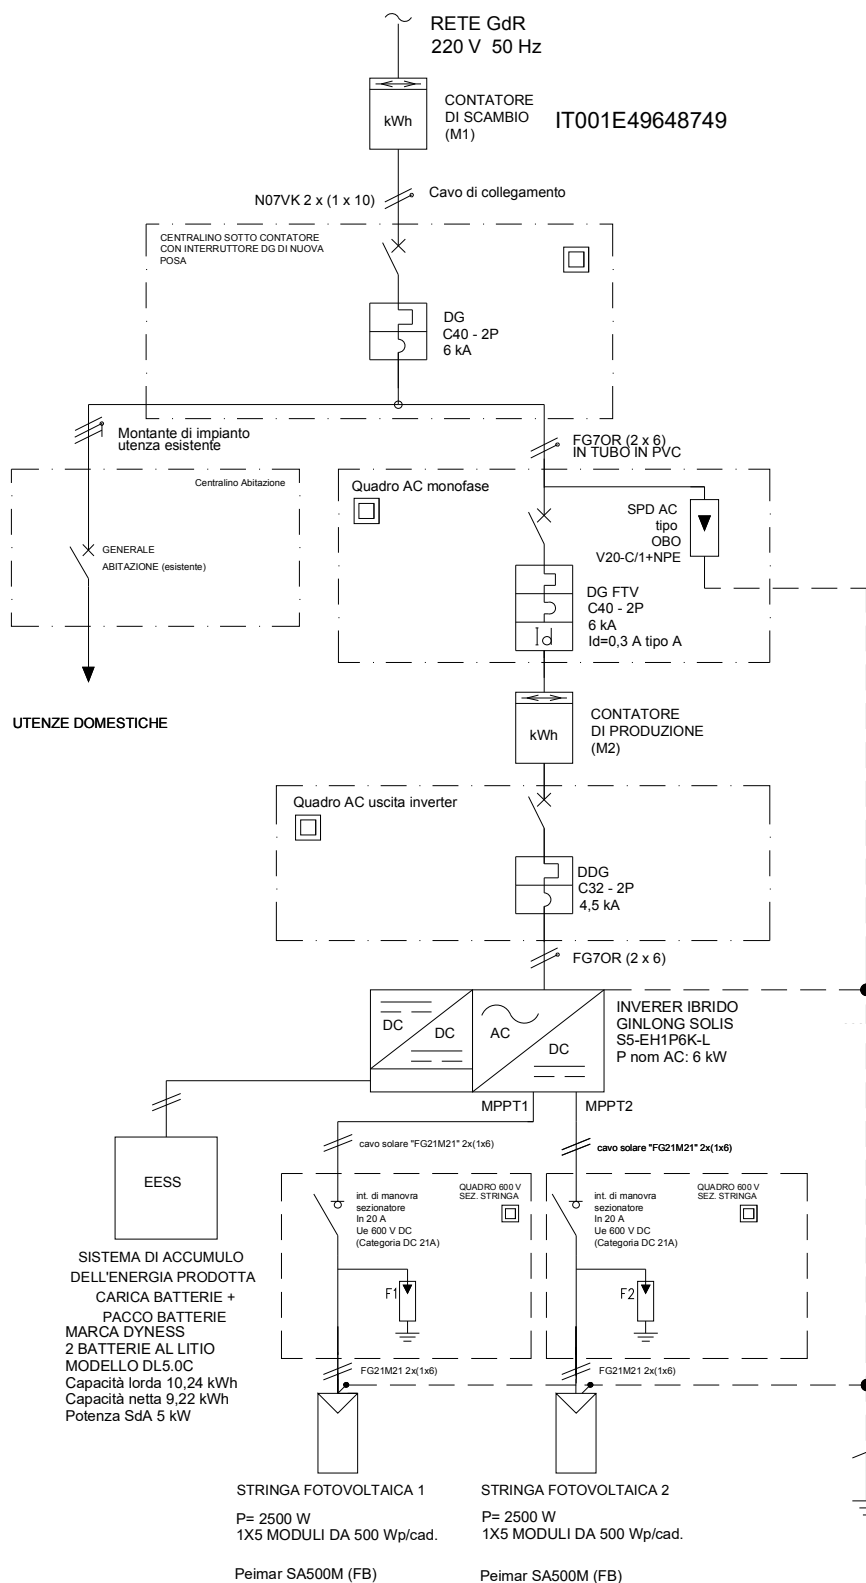

NB:

Esula dallo scopo del presente progetto i calcoli della struttura di sostegno dei moduli fotovoltaici e l'analisi della portata della copertura dell'edificio allo stato di fatto. Sarà cura della ditta installatrice verificare sia in sopralluogo che in corso d'opera lo stato del tetto (per valutare la necessità di una verifica statica) e dell'impianto di terra per permettere il corretto funzionamento dell'impianto, degli interruttori differenziali e degli SPD (ai sensi e per gli effetti del D.M. 37/08)

Si consiglia di collegare a terra la struttura di sostegno dei moduli FV al fine di consentire un corretto funzionamento del sistema di controllo dell'isolamento implementato nel convertitore.

La scelta della componentistica elettrica dovrà rispettare le indicazioni riportate nel seguente schema, ed i centralini avere un indice di protezione pari o superiore a IP65 ed essere isolati.

Al Progettista non potrà essere attribuita alcuna responsabilità circa le scelte progettuali qualora nella realizzazione dell'impianto vengano apportate modifiche, ampliamenti o diminuzioni ai lavori indicati negli schemi elettrici e/o planimetrici ed eventuali relazioni.

In caso di varianti significative in corso d'opera per necessità impiantistiche o altre particolari esigenze dovrà essere preventivamente inviata comunicazione scritta al Progettista il quale provvederà a verificare, sia le nuove condizioni dell'impianto che la sicurezza dello stesso, nonché la loro incidenza sulla sicurezza generale.



[Handwritten signature]

PROGETTISTA: Ing. Alessandro Zuanetti

COMMITTENTE:

INDIRIZZO: VIA MASSA 26
60010 OSTRÀ(AN)

TITOLO: Schema unifilare preliminare

CHIU' GIANNI

DATA: 14/11/2025

FOGLIO: 1 di 1