


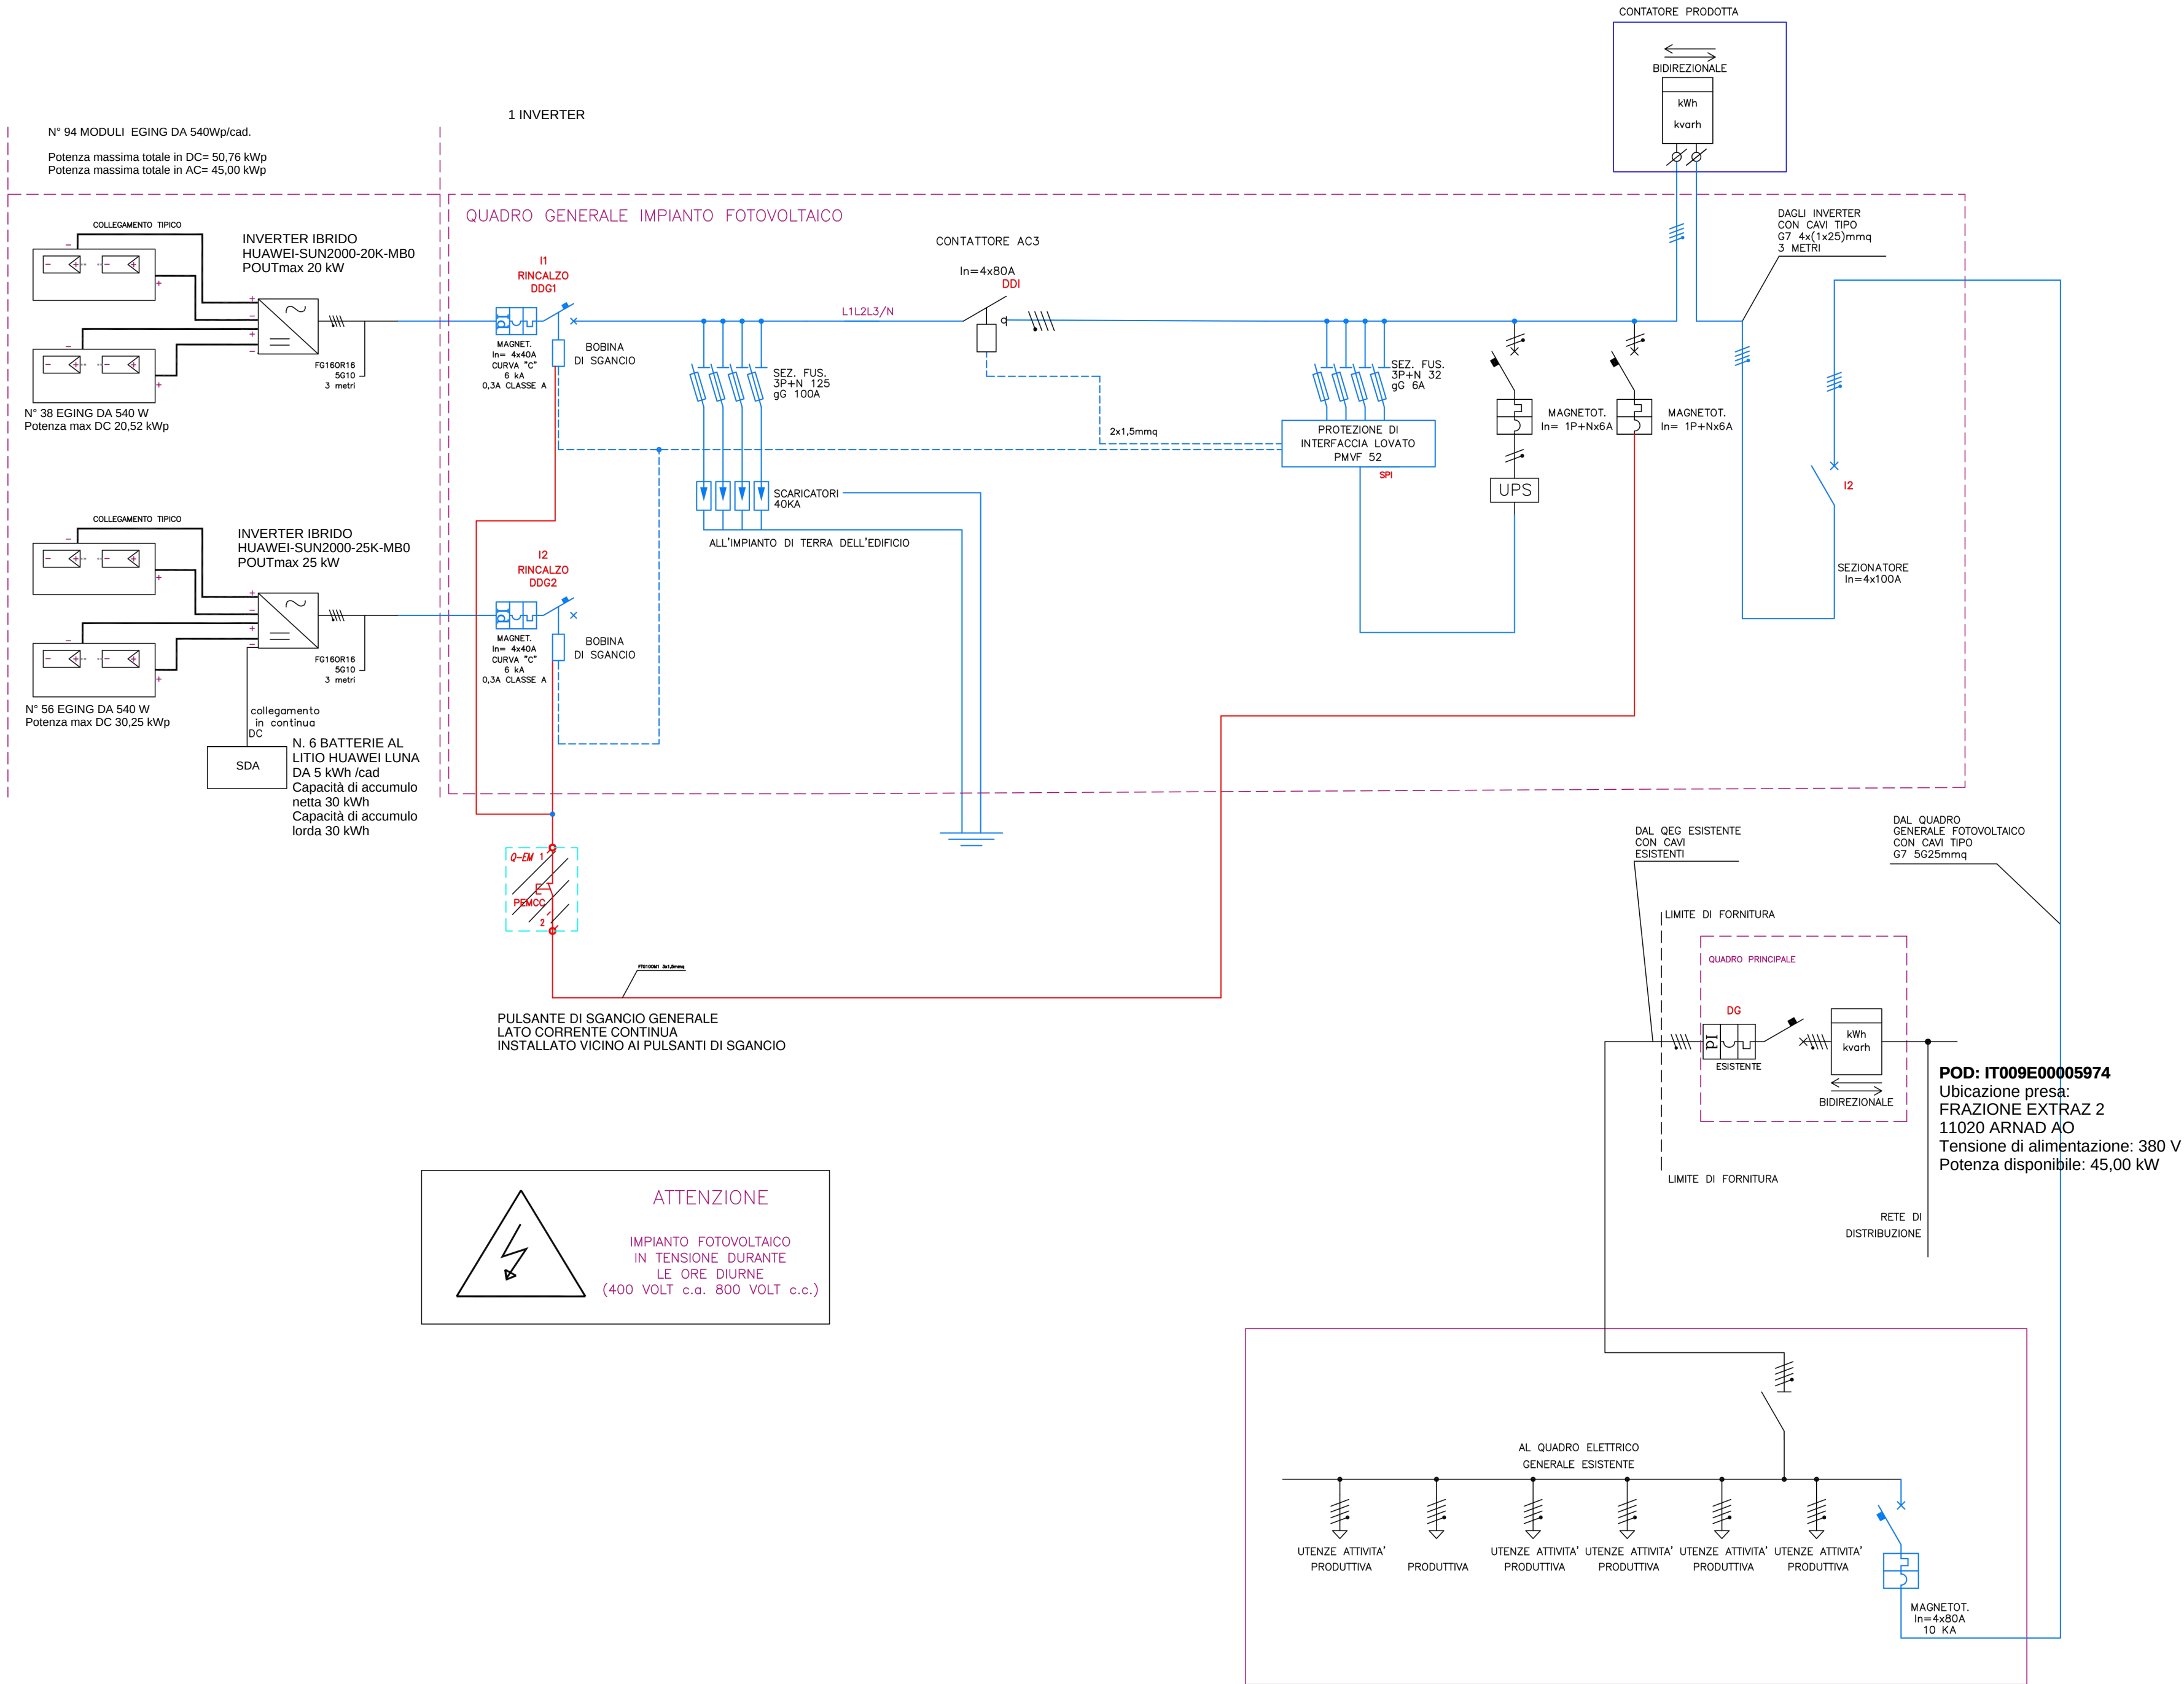

AZING

SRL

INGEGNERIA

Committente	LARDIFICIO PIETRO LAURENT	Fase progetto	PRELIMINARE
		Categoria lavoro	PRELIMINARE
Indirizzo	FRAZIONE EXTRAZ 3 11020 ARNAD AO	Tavola	01
		Piano/scala	-
Oggetto	SCHEMA IMPIANTO FOTOVOLTAICO	Revisione	00
Descrizione	UNIFILARE IMPIANTO	Disegnatore	A.Z.
Progettista	ING. ALESSANDRO ZUANETTI		

REV	DATA	DESCRIZIONE	VER	DATA	VAL	DATA
00	18/10/25	UNIFILARE	A.Z.	18/10/25	A.Z.	18/10/25

Il presente disegno è di proprietà riservata. E' vietata la riproduzione senza autorizzazione