


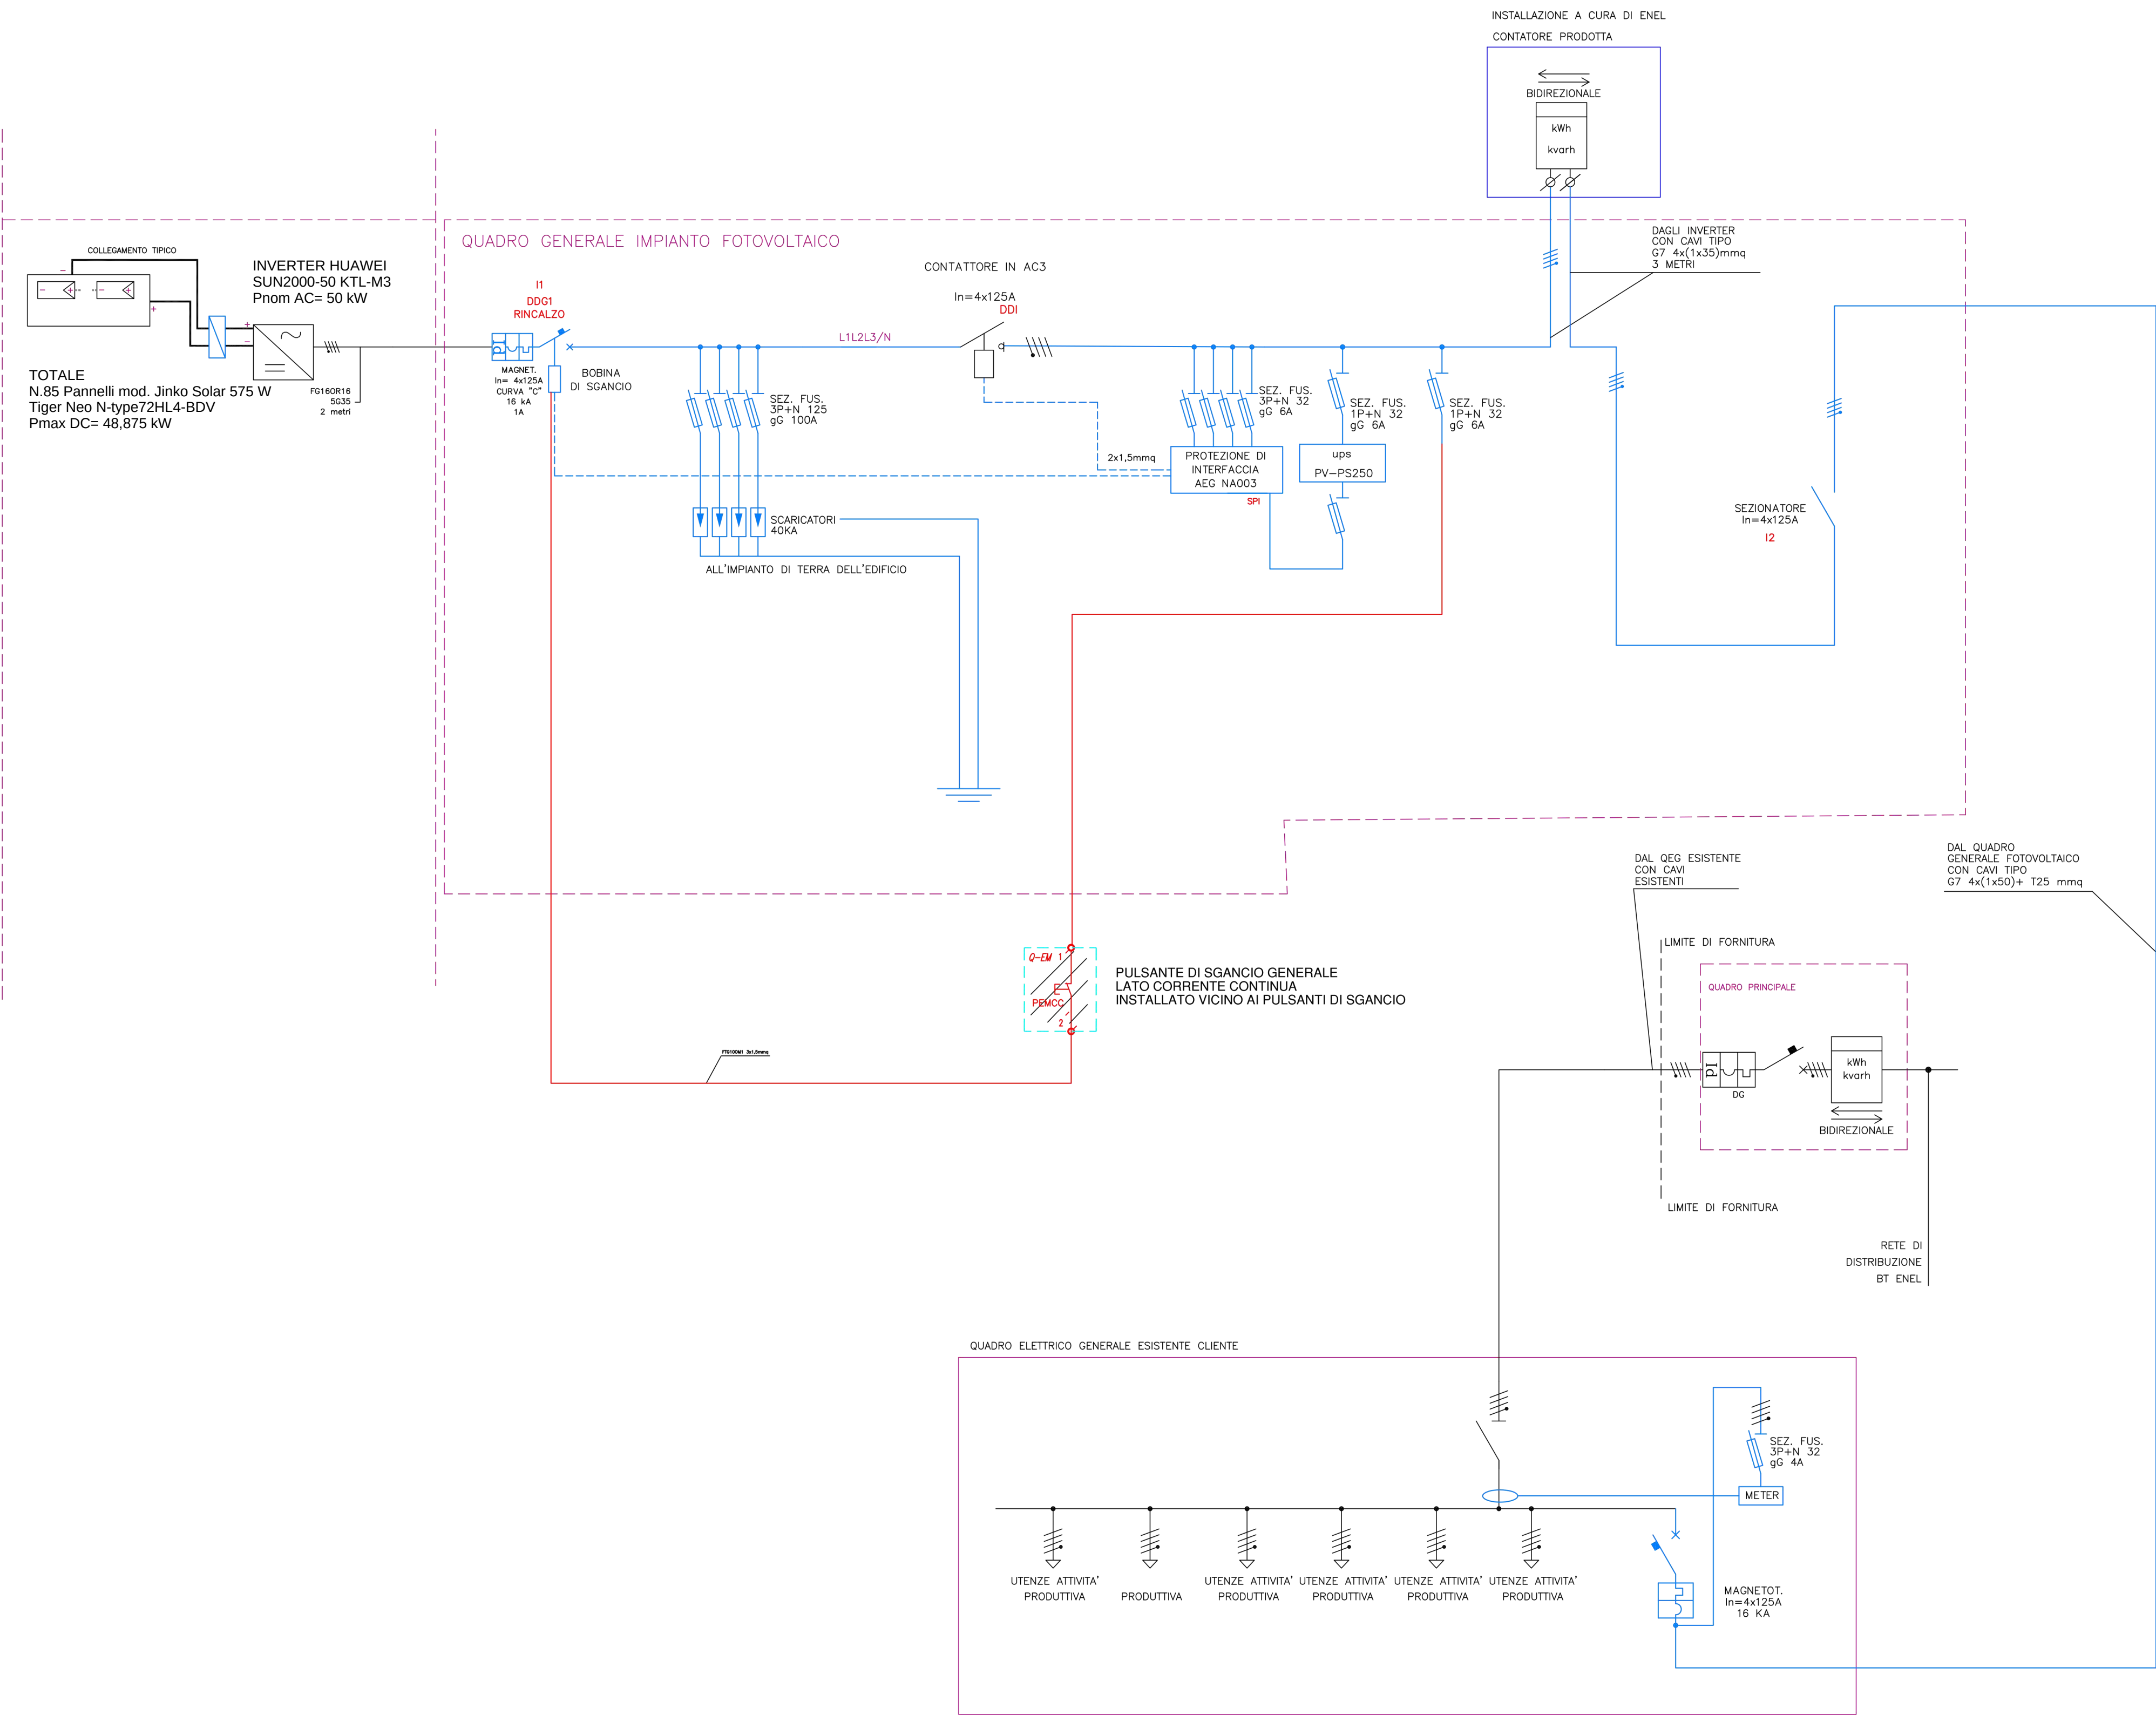

ATTENZIONE

IMPIANTO FOTOVOLTAICO
IN TENSIONE DURANTE
LE ORE DIURNE
(400 VOLT c.a. 800 VOLT c.c.)

AZING

SRL

INGEGNERIA

Committente	DIMAGO S.r.l.	Fase progetto	PRELIMINARE
	Indirizzo	LUNGOMARE G. MATTEOTTI 157 MELENDUGNO (LE)	Categoria lavoro
Oggetto		PROGETTO IMPIANTO FOTOVOLTAICO	Tavola
	Descrizione	PRELIMINARE	Piano/scala
Progettista		ING. ALESSANDRO ZUANETTI	Revisione
			Disegnatore

REV	DATA	DESCRIZIONE	VER	DATA	VAL	DATA
00	23/09/25	UNIFILARE	A.Z.	23/09/25	A.Z.	23/09/25

Il presente disegno è di proprietà riservata. E' vietata la riproduzione senza autorizzazione

